King County
Department of Permitting and Environmental Review

COVER SHEET AND SITE PLAN

Ref: KCC 21a.12.030

Max. Impervious Surface Allowed	255,479 SF
Max. Bldg. Height Allowed	35 FEET

Ref: KCC 21a.12.170

Min. Blg. Setback From Street	30 FEET
Min. Garage Setback From Street	30 FEET
Min. Blg. Setback From Interior	5 FEET

Permit Center validation:

- o Zoning
- o Site Review Not Applicable

Validated Signature _____

Login Initials _____ Date: _____

Critical Areas Approval

Signature: _____

Date: _____

Fire Approval

Signature: _____

Date: _____

Engineering / Drainage Approval

Signature: _____

Date: _____

Clearing / Grading Approval

Signature: _____

Date: _____

GRAPHIC SCALE
0 75 150 300
1 INCH = 150 FEET (11x17)

THIS IS NOT A SURVEY, TOPOGRAPHICAL INFORMATION SHOWN HERE PER AVAILABLE LIDAR.

APPLICANT
PRESIDENTIAL HOMES LLC
1212 39TH AVE SW
PUYALLUP, WA 98373
PH: (253) 256-4271

ARCHITECT
LANDMARK DESIGN
1202 MAIN ST. SUITE #104
SUMNER, WA 98390
PH: (253) 826-7808

CIVIL ENGINEER
CONTOUR ENGINEERING LLC
4706 97TH STREET NW, STE 100
P.O. BOX 949
GIG HARBOR, WA 98335
PH: (253) 857-5454

SEPTIC DESIGNER
ROBERT GOODMAN
P.O. BOX 64387
UNIVERSITY PLACE, WA 98464
PH: (253) 584-1794

LEGAL DESCRIPTION
THE SOUTHEAST QUARTER OF SECTION 22, TOWNSHIP 20 NORTH, RANGE 06 EAST, W.M., IN KING COUNTY, WASHINGTON

PROJECT INFORMATION

ADDRESS:	236XX SE 448TH ST. ENUMCLAW, WA 98022
PARCEL NUMBER:	2220069212
JURISDICTION:	KING COUNTY
ZONING:	URBAN RESERVE SPECIAL DISTRICT OVERLAY (UR - SO)
TOTAL SITE AREA:	851,598 SQ. FT. (19.55 AC)
TOTAL IMPERVIOUS:	10,824 SF (0.25 AC, 1.27% OF PARCEL)
	ROOF AREA = 3,220 SQ. FT.
	WALKWAY = 98 SQ. FT.
	DRIVEWAY = 7,506 SQ. FT.

SITE PLAN NOTES
1. PROPOSED FEATURES, STRUCTURE LOCATIONS, AND TOPOGRAPHIC INFORMATION ARE BASED ON INFORMATION PROVIDED BY THE CLIENT, SEPTIC DESIGNER, AND PER SITE INSPECTION.
2. CLIENT IS TO REVIEW SITE PLAN WITH CONTRACTOR PRIOR TO ANY CONSTRUCTION AND VERIFY ALL EXISTING AND PROPOSED INFORMATION.
3. ADJUSTMENTS AND/OR REVISIONS TO SITE LAYOUT, BUILDING FOOTPRINT AND/OR BUILDING ORIENTATION MAY RESULT IN THE NEED TO REVISE THESE PLANS ACCORDINGLY OR PER COUNTY INSPECTOR.

CONTRACTOR NOTE
ALL EXISTING UTILITIES SHOWN ON PLANS ARE TO BE VERIFIED HORIZONTALLY AND VERTICALLY PRIOR TO ANY CONSTRUCTION. ALL EXISTING FEATURES INCLUDING BURIED UTILITIES ARE SHOWN AS INDICATED ON RECORD MAPS AND SURVEY FURNISHED BY OTHERS. WE ASSUME NO LIABILITY FOR THE ACCURACY OF THOSE RECORDS AND SURVEY, FOR THE FINAL LOCATION OF EXISTING UTILITIES IN AREAS CRITICAL TO CONSTRUCTION CONTACT THE UTILITY OWNER/AGENCY.

SURVEY INFORMATION NOTES
1. NO TOPOGRAPHIC SURVEY WAS PERFORMED FOR THE SITE. ALL TOPOGRAPHIC INFORMATION DEPICTED IS DERIVED FROM LIDAR INFORMATION OBTAINED FROM KING COUNTY GIS.
2. NO BOUNDARY SURVEY WAS PERFORMED AND NO TITLE REPORT WAS PROVIDED. ALL PROPERTY LINES AND EASEMENTS DEPICTED ARE BASED UPON INFORMATION OBTAINED FROM KING COUNTY ASSESSORS OFFICE.
3. CLIENT AND CONTRACTOR SHALL REVIEW ALL THE SURVEY INFORMATION SHOWN PRIOR TO CONSTRUCTION AND VERIFY ALL EXISTING INFORMATION. CONTACT CONTOUR ENGINEERING IF ANY CONFLICTS ARISE OR IF SOME INFORMATION IS SHOWN INCORRECTLY BASED ON FIELD VERIFICATION.

FILL SPECIFICATION
FILL MATERIAL SHALL NOT CONTAIN PETROLEUM PRODUCTS, OR SUBSTANCES WHICH ARE HAZARDOUS, DANGEROUS, TOXIC, OR WHICH OTHERWISE VIOLATE ANY STATE, FEDERAL, OR LOCAL LAW ORDINANCE, CODE, REGULATION, RULE, ORDER, OR STANDARD. ONLY EARTH MATERIAL SHALL BE PLACED IN FILLS.

SHEET INDEX

1 of 4	SITE PLAN
2 of 4	TESC PLAN
3 of 4	GRADING AND DRAINAGE PLAN
4 of 4	DRIVEWAY CROSS SECTION

LEGEND

SURVEY		PROPOSED
100	CONTOURS	100
	PROPERTY LINE/RIGHT-OF-WAY	
	BUILDING SETBACK	
	ROOF DRAIN LINE	RD
	SANITARY SEWER LINE	SS
	WATER LINE	W
	TYPE 1/TYPE 1L CATCHBASIN	
	STORM DRAIN CLEANOUT (SDCO)	
	VEGETATED FLOWPATH	
	GRAVEL	
	ASPHALT	

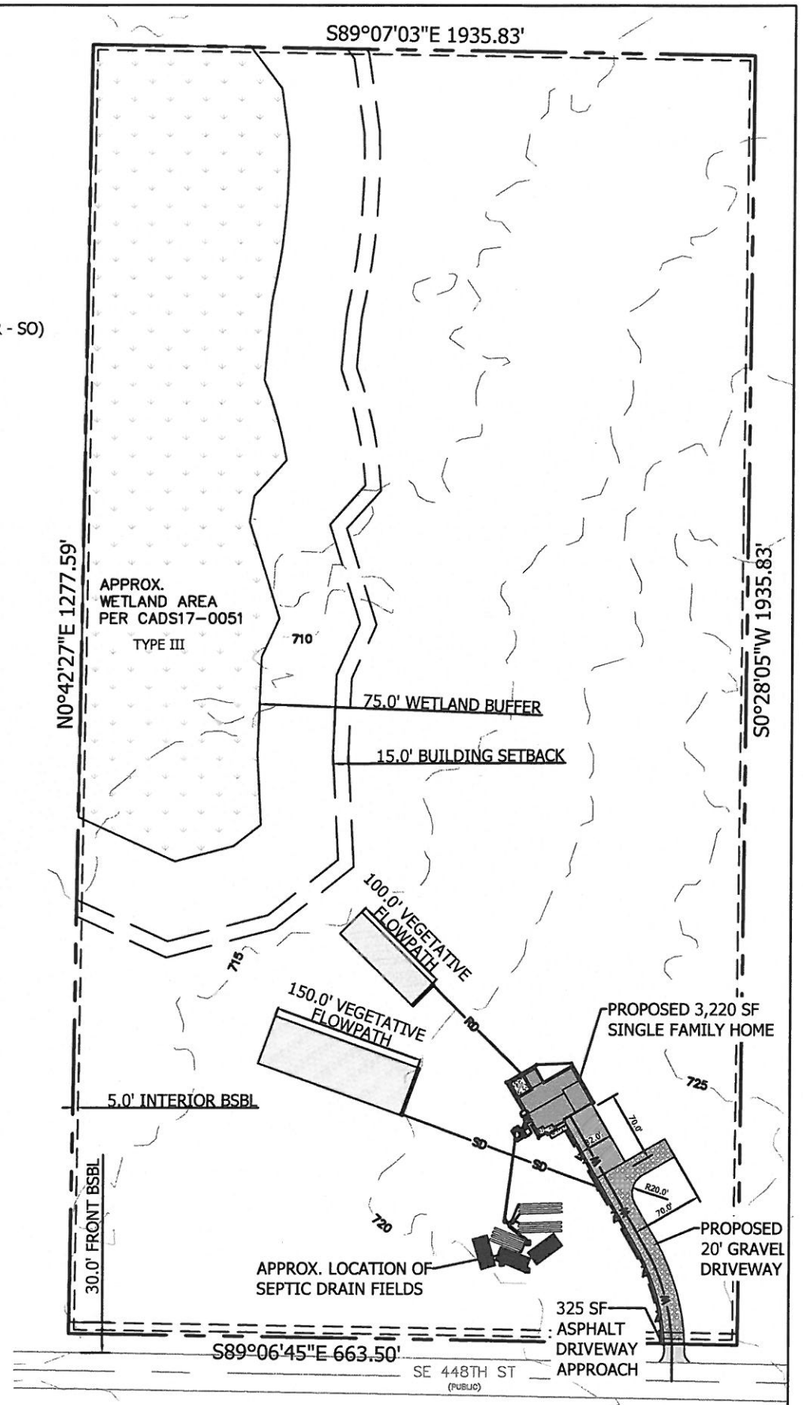

Permit Number: _____ Parcel Number: 222006-9212 Applicant Name: PRESIDENTIAL HOMES LLC Site Address: 236XX SE 448TH ST. ENUMCLAW, WA 98022

Engineering Scale: 1" = 150'